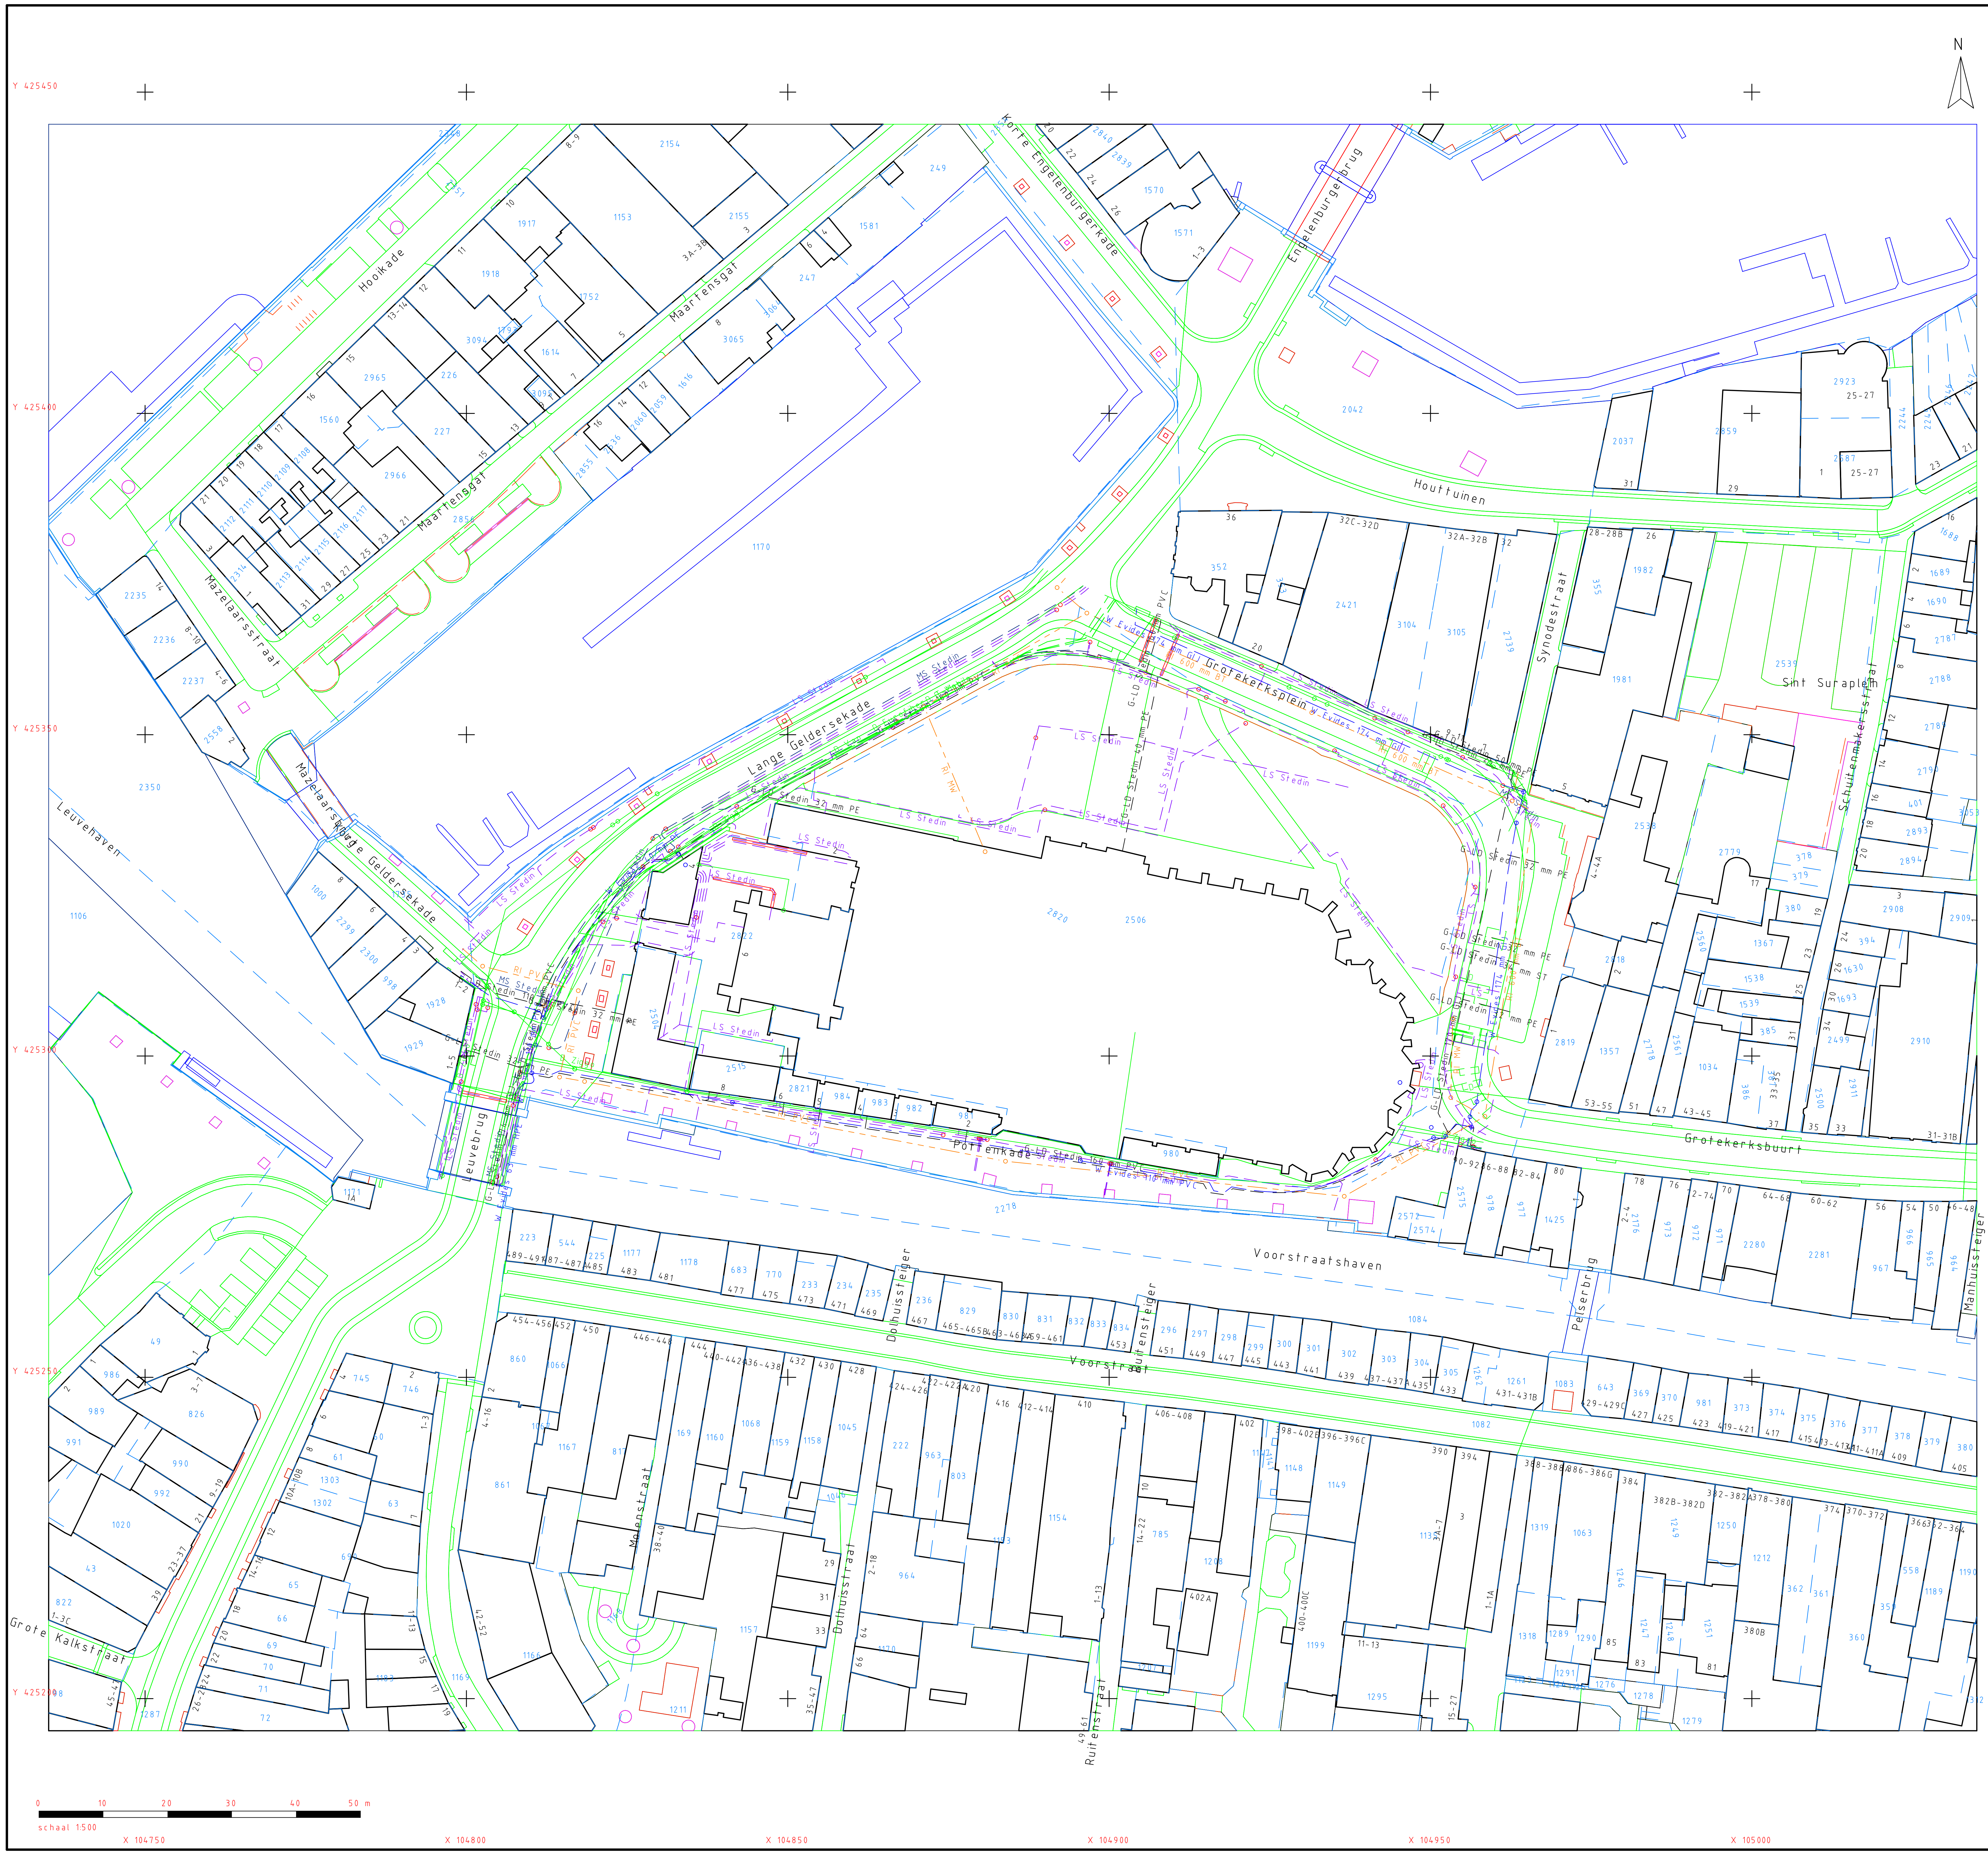
N
Y 425450
Y 425400
Y 425350
Y 425300
Y 425250
Y 425200
X 104750
X 104800
X 104850
X 104900
X 104950
X 105000
0
10
20
30
40
50 m
schaal 1:500
Hooikade
Maartensgat
Korte Engelenburgerkade
Engelenburgerbrug
Houttuinen
Grotekerksplein
Synodestraat
Sint Suraplein
Schuitenmakersstraat
Lange Geldersekade
Mazelaarsstraat
Leuvehaven
Leuvebrug
Pottenkade
Grotekerksbuurt
Voorstraatshaven
Voorstraat
Dolhuissteiger
Pelserbrug
Manhuissteiger
Molenstraat
Dolhuisstraat
Ruitenstraat
Grote Kalkstraat

LEGENDA

GK — GrondKeringen
- Kademuur

GR — GRoen
- Beplanting cultuur bodembedekker
- Beplanting cultuur heesters
- Beplanting cultuur roos
- Beplanting cultuur vaste plantenvak
- Groenvoorziening
- Struik

IE — InrichtingsElementen
- Terreinafscheiding kunstmatig hekwerk
- Terreinafscheiding kunstmatig muur

KG — Kadastrale informatie en Grenzen
- Grens perceel

KL — Kabels en Leidingen
- ○ Data hulpstuk
- Data mantelbuis
- Data telecom
- ○ Et hulpstuk
- Et ls
- Et mantelbuis
- Et ms
- ○ Gas hulpstuk
- Gas ld
- ○ Water hulpstuk
- Water transportleiding

KW — KunstWerken
- Kunstwerk
- Kunstwerk dek
- Kunstwerk pijler
- Kunstwerk steiger

OG — OnderGrond
- Bebouwing
- Bebouwing bordes
- Bebouwing overbouwing
- Bebouwing trap
- Terrein erf
- Terrein oever
- Water
- Water haven
- Water rivier

RI — RIolering
- Gwa rioolleiding
- ○ Gwa rioolput

VH — VerHardingen
- Geslotenverharding
- Geslotenverharding asfalt
- Geslotenverharding beton
- Geslotenverharding kunststof
- Onverhard zand
- Openverharding
- Openverharding betonstraatsteen
- Openverharding sierbestrating
- Openverharding straatbaksteen
- Openverharding tegel

OPEN INFRA
OpenAEC Foundation — Open CAD Studio

NLCS 5.02

project
Dordrecht, Grote Kerk

onderwerp
Situatie bestaand - BGT, kadaster en kabels en leidingen

schaal 1:500	datum 24-10-2026	getekend Open Infra	discipline XX
tekeningnummer OI-001	tekenstatus B — bestaand	coördinatenstelsel EPSG:28992	formaat A1 liggend

bronnen
BGT (PDOK, CC0) · BRK kadastrale kaart (Kadaster, CC BY 4.0) · KLIC-levering 210072584 (Kadaster)